


CSD/SEM

前置作業提醒：


1. 主檔與連結檔案，**Level 名稱需與主檔相符**，否則會導致開口對應不到正確的 Level 無法寫入參數。
2. 連結檔名請以 **-** 分隔命名：OOO-XX-OO.rvt，例：D-AR-LG10-B.rvt。
3. 族群名稱包含帷幕牆、輕隔間、珞瑯、廁所隔牆，**不會**進行開口、套管放置。

自動開口：


1. 載入要進行管道與建築開口的模型。

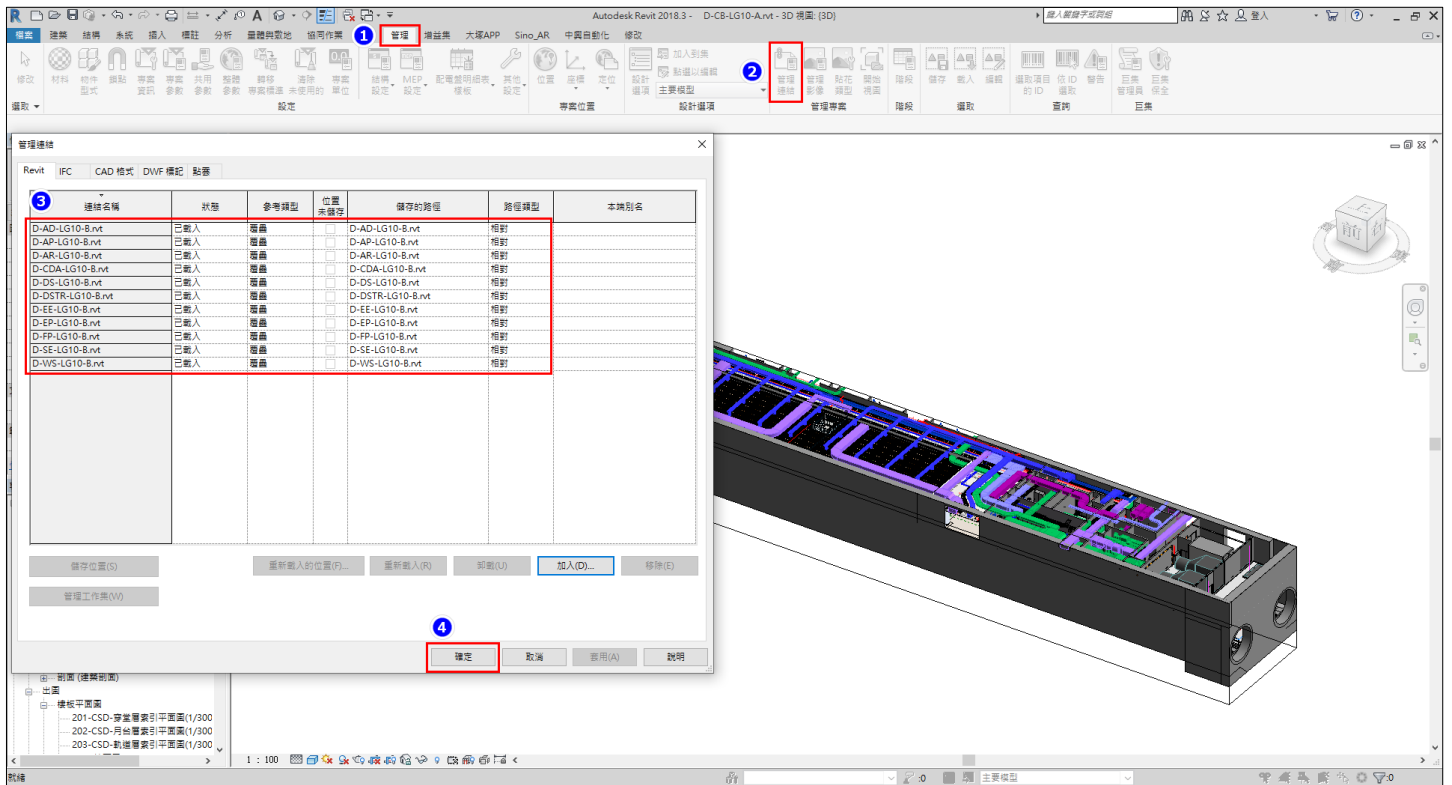


2. 載入外掛安裝檔中提供的開口族群與標籤。

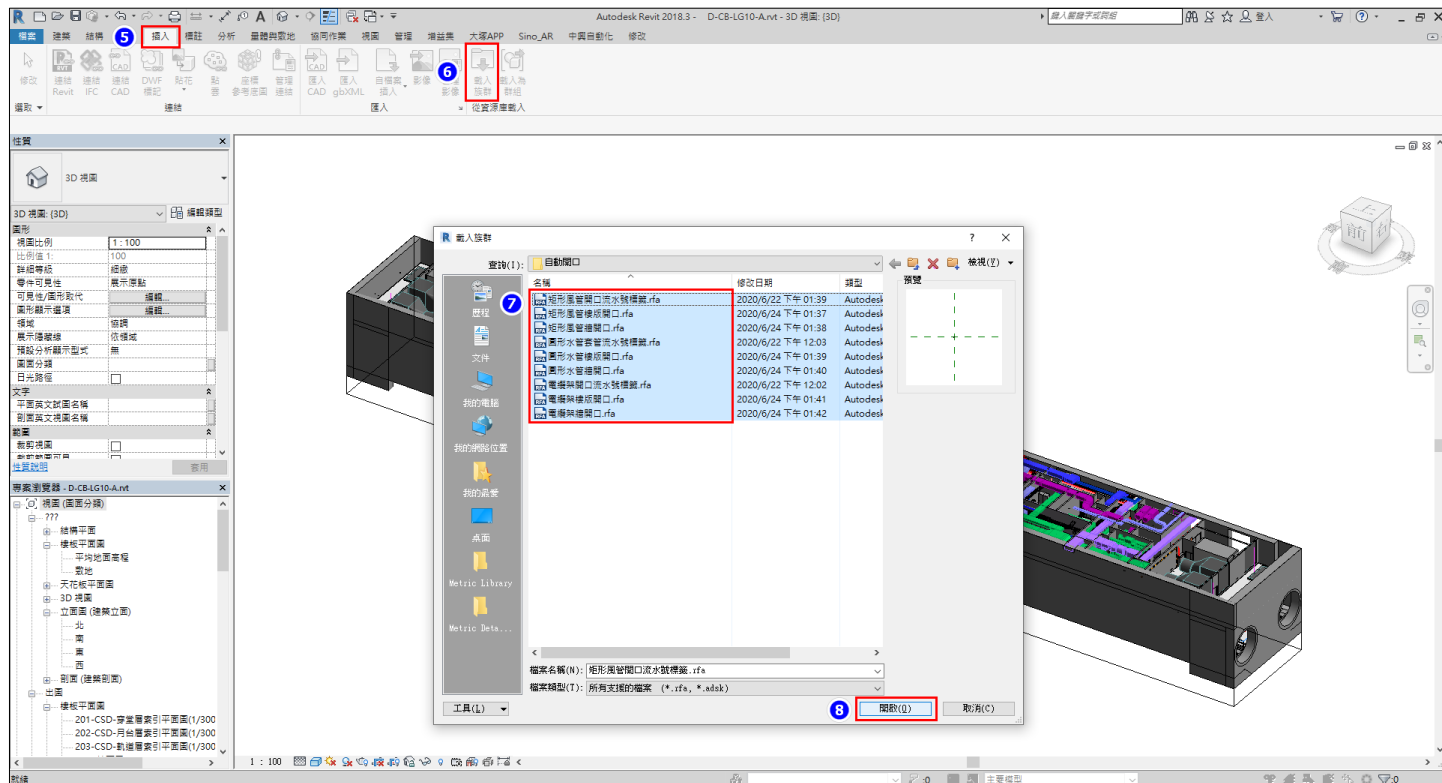

3. 點選自動開口，自動運算管道與建築干涉的部分，進行開口、套管放置。

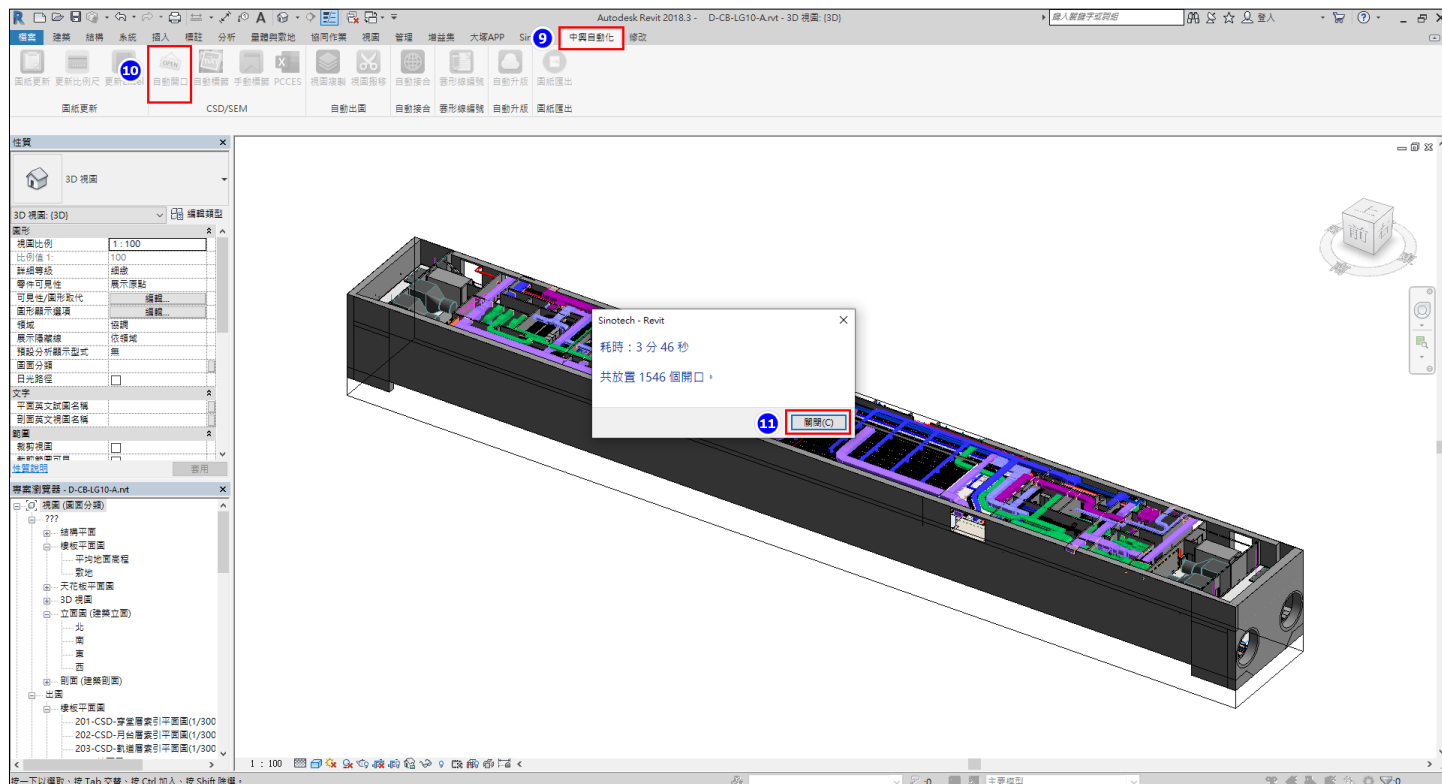


4. 依管徑自動調整開口類別、大小與方向。


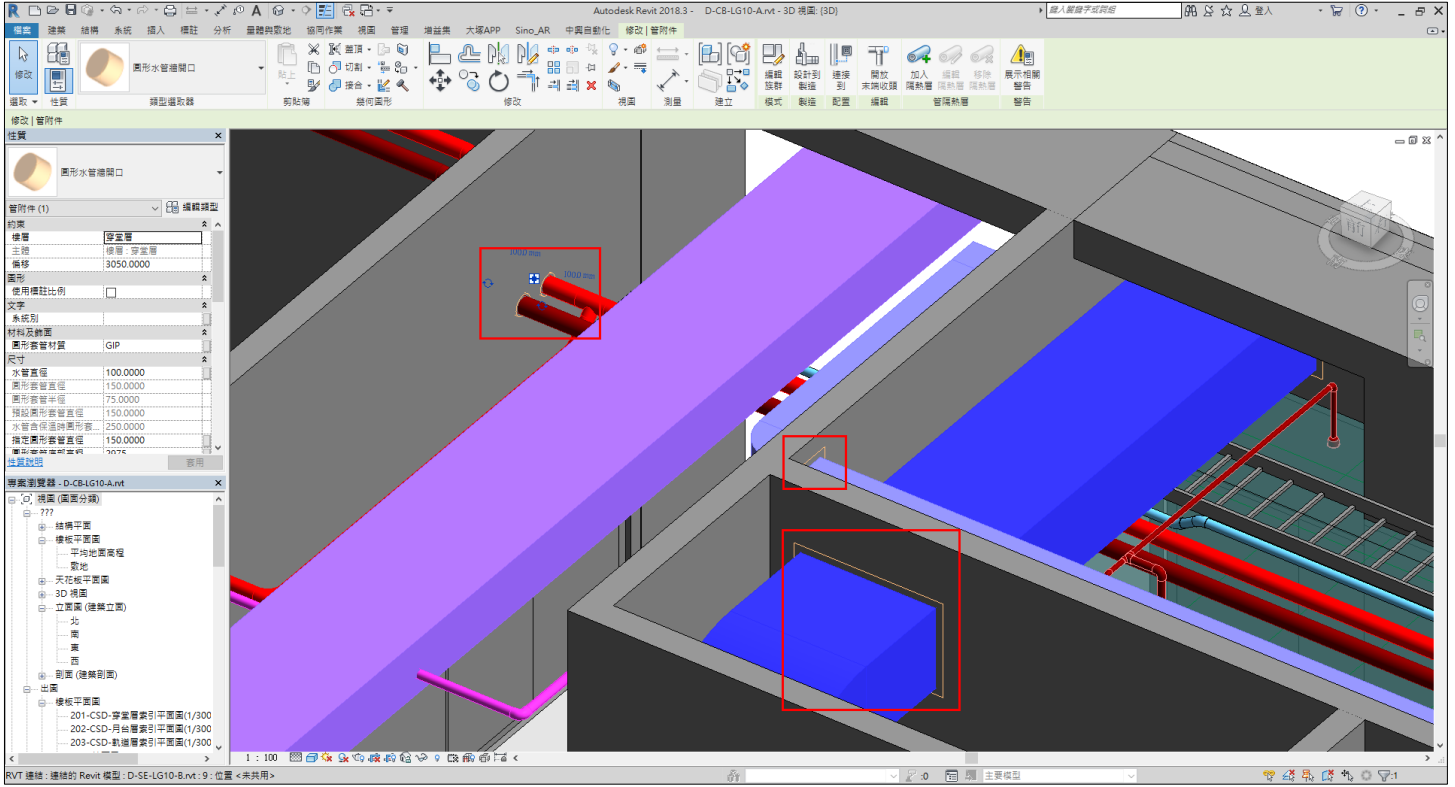


自動標籤：

1. 為載入的自動開口族群加上標籤。

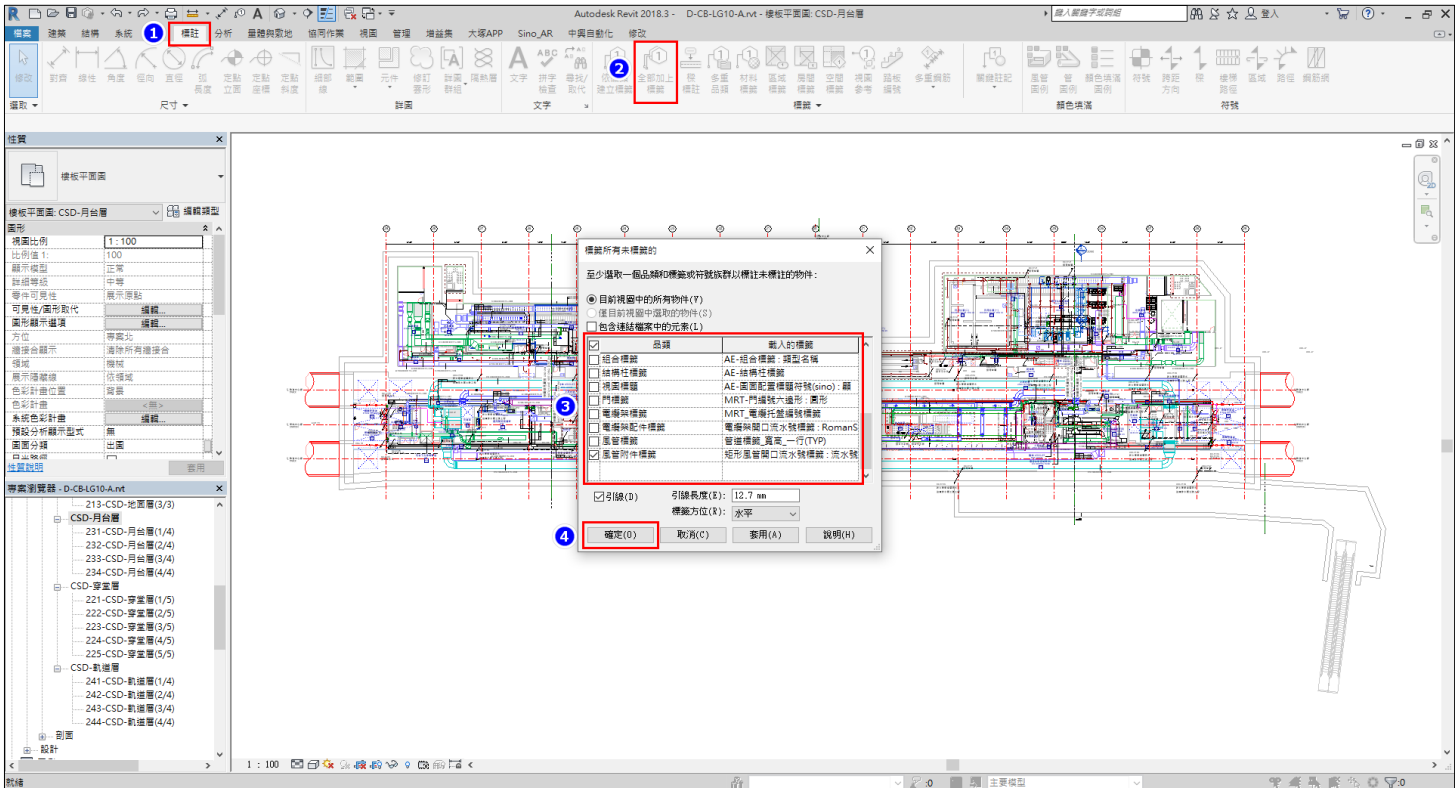


2. 自動依樓層、系統、管道動線進行編號。

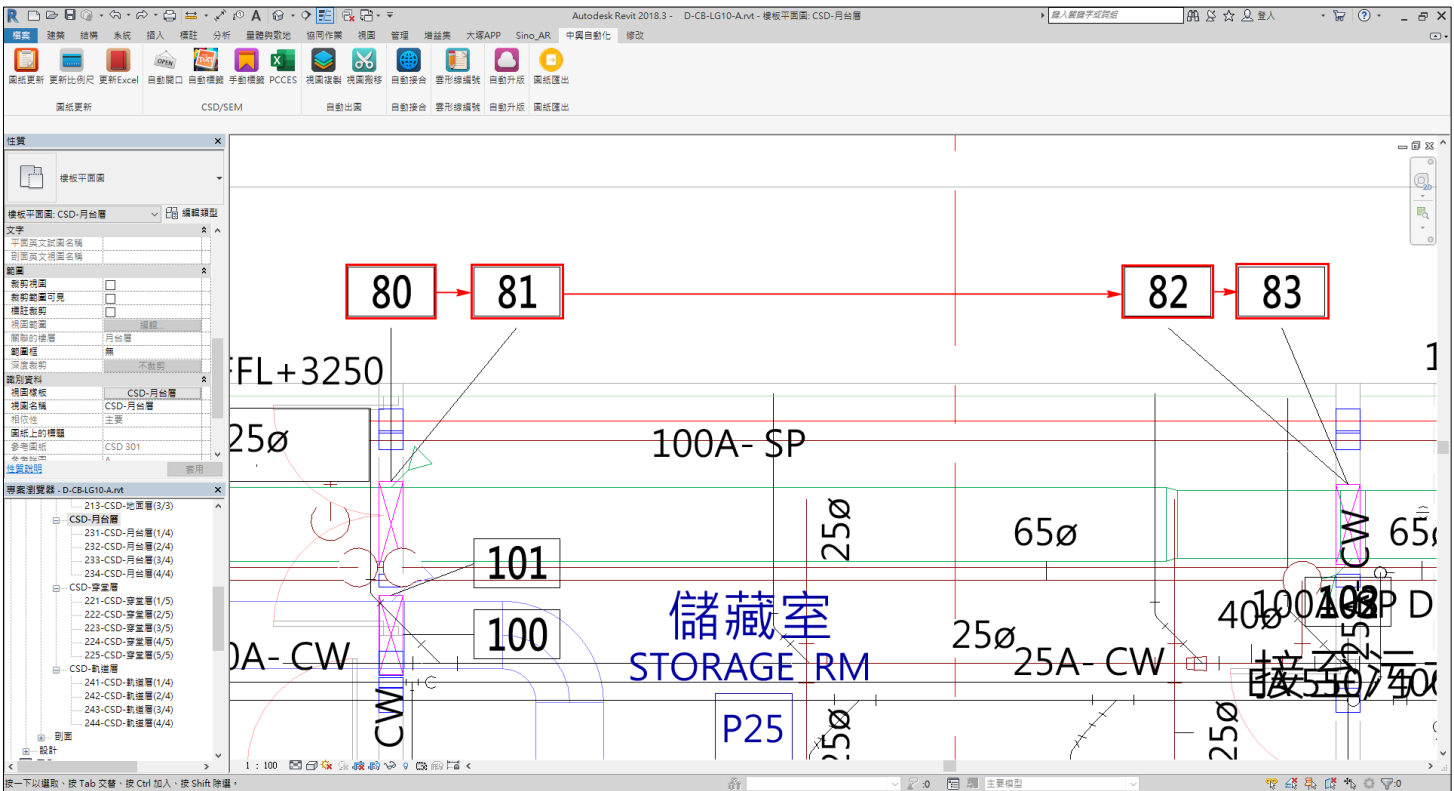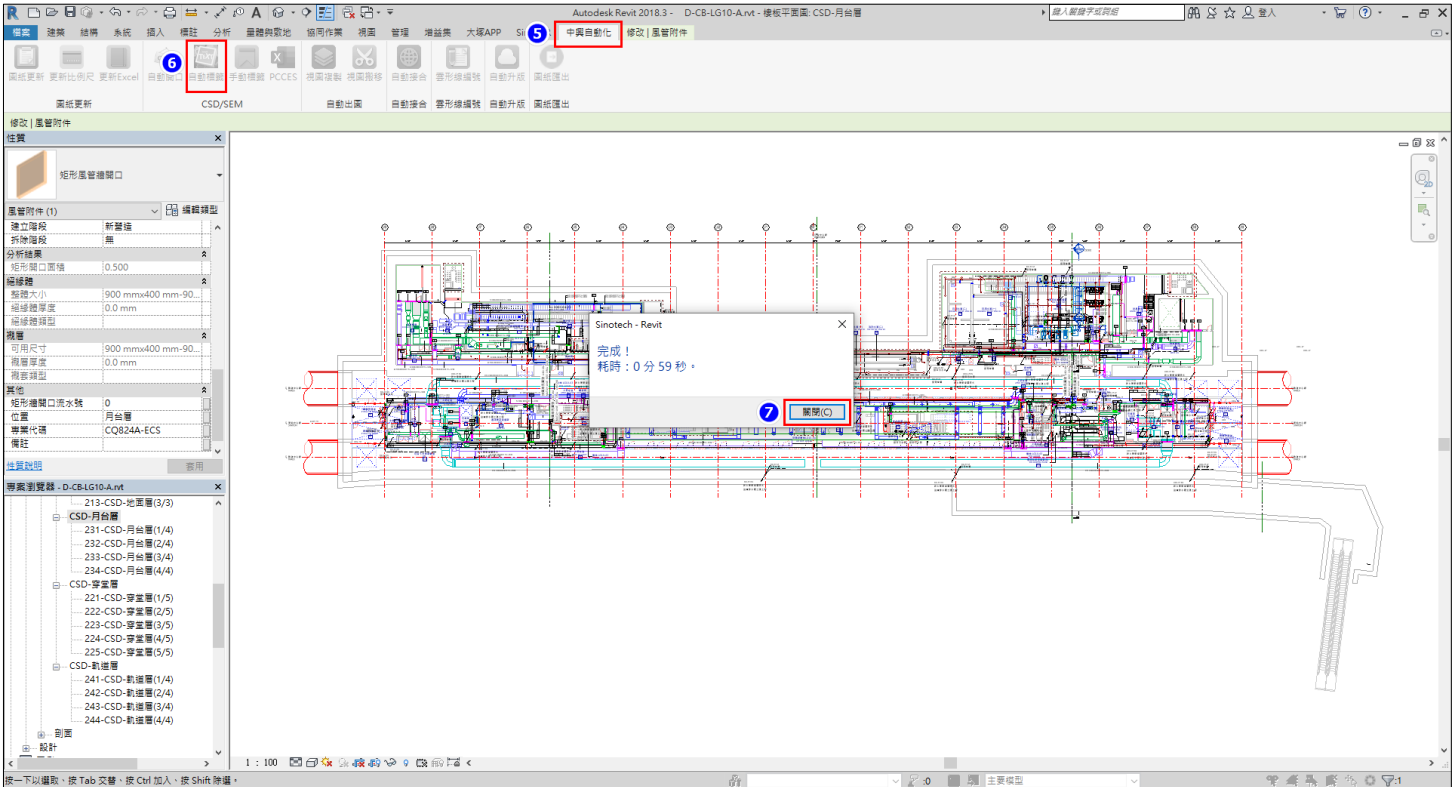


手動編號：

1. 輸入起始編號。

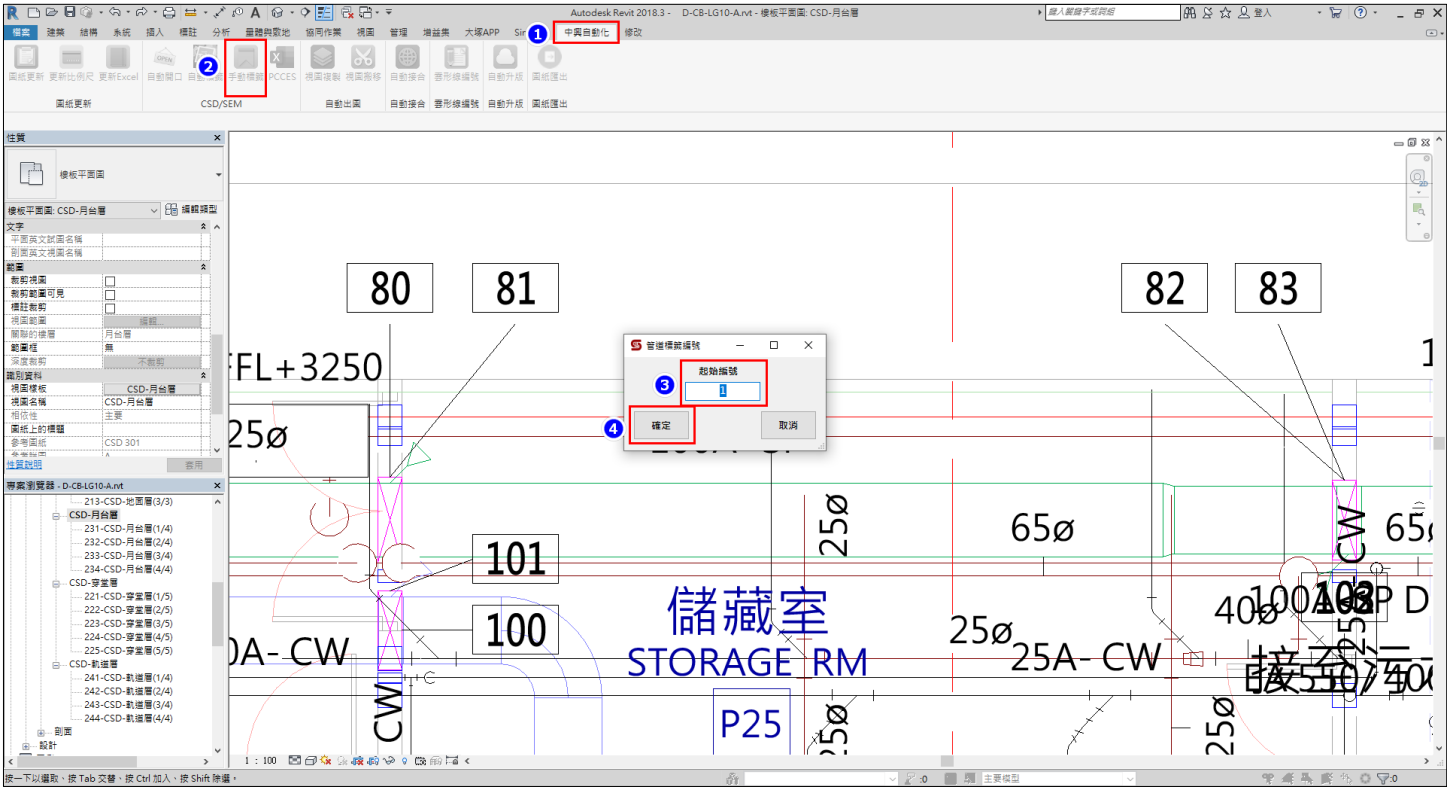


2. 點選要進行編號的開口，完成時按鍵盤 Esc 鍵退出。

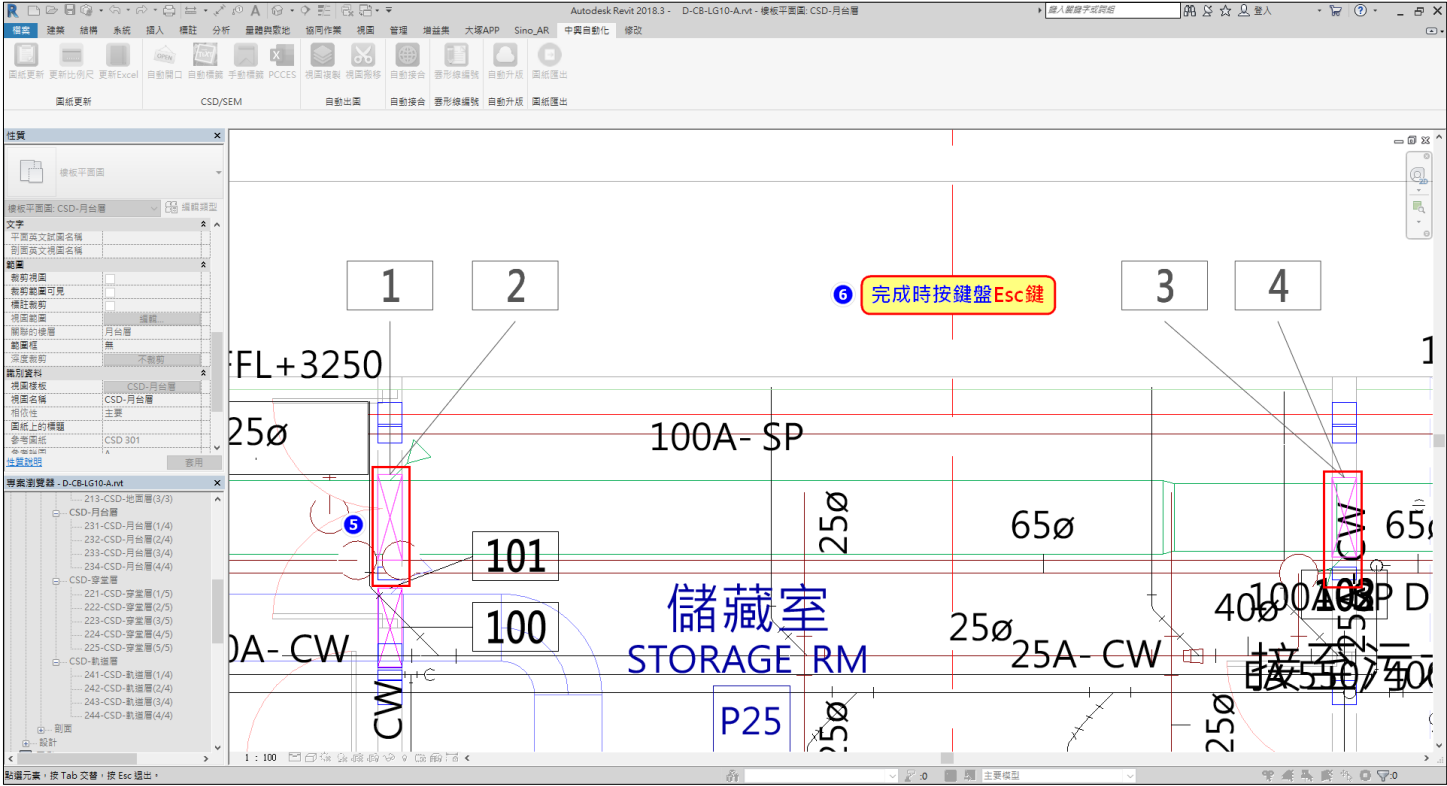


1. 開啟工程數量詳細表.xlsx，於 detail、All 中，輸入要比對的配件名稱與項目編號。

項次	配合其他系統標	量(彙總計算)	參考頁次	工程項目編號
A1	配合CG390C水電環控及監控施工標			
A2	配合CG396E電扶梯電梯施工標			
A3	配合CG396E電扶梯電梯施工標			
A1-01	管及管件, PVC管(B管厚管), (標稱50mm, 厚4.1mm), 樓板套管裝設	個		151053072#
A2-01	管及管件, PVC管(B管厚管), (標稱65mm, 厚4.1mm), 樓板套管裝設	個		151053082#
A3-01	管及管件, PVC管(B管厚管), (標稱80mm, 厚5.1mm), 樓板套管裝設	個		151053092#
	管及管件, PVC管(B管厚管), (標稱100mm, 厚6.6mm), 樓板套管裝設	個		1510530B2#
	管及管件, 配管用碳鋼鋼管, 鍍鋅鋼管, (標稱50mm, 厚3.8mm), 牆套管裝設	個		151054291#
	管及管件, 配管用碳鋼鋼管, 鍍鋅鋼管, (標稱65mm, 厚4.2mm), 牆套管裝設	個		1510542A1#
	管及管件, 配管用碳鋼鋼管, 鍍鋅鋼管, (標稱80mm, 厚4.2mm), 牆套管裝設	個		1510542B1#
	管及管件, 配管用碳鋼鋼管, 鍍鋅鋼管, (標稱100mm, 厚4.5mm), 牆套管裝設	個		1510542D1#
	管及管件, 配管用碳鋼鋼管, 鍍鋅鋼管, (標稱125mm, 厚4.5mm), 牆套管裝設	個		1510542E1#
	管及管件, 配管用碳鋼鋼管, 鍍鋅鋼管, (標稱150mm, 厚5.0mm), 牆套管裝設	個		1510542F1#
	管及管件, 配管用碳鋼鋼管, 鍍鋅鋼管, (標稱200mm, 厚5.8mm), 牆套管裝設	個		1510542H1#
	管及管件, 配管用碳鋼鋼管, 鍍鋅鋼管, (標稱250mm, 厚6.6mm), 牆套管裝設	個		1510542K1#
	管及管件, 配管用碳鋼鋼管, 鍍鋅鋼管, (標稱300mm, 厚6.9mm), 牆套管裝設	個		1510542L1#
	管及管件, 配管用碳鋼鋼管, 鍍鋅鋼管, (標稱350mm, 厚7.9mm), 牆套管裝設	個		1510542M1#
	管及管件, 配管用碳鋼鋼管, 鍍鋅鋼管, (標稱400mm, 厚7.9mm), 牆套管裝設	個		1510542N1#
	管及管件, 配管用碳鋼鋼管, 鍍鋅鋼管, (標稱50mm, 厚3.8mm), 樓板套管裝設	個		151054293#
	管及管件, 配管用碳鋼鋼管, 鍍鋅鋼管, (標稱65mm, 厚4.2mm), 樓板套管裝設	個		1510542A3#
	管及管件, 配管用碳鋼鋼管, 鍍鋅鋼管, (標稱80mm, 厚4.2mm), 樓板套管裝設	個		1510542B3#
	管及管件, 配管用碳鋼鋼管, 鍍鋅鋼管, (標稱100mm, 厚4.5mm), 樓板套管裝設	個		1510542D3#
	管及管件, 配管用碳鋼鋼管, 鍍鋅鋼管, (標稱125mm, 厚4.5mm), 樓板套管裝設	個		1510542E3#
	管及管件, 配管用碳鋼鋼管, 鍍鋅鋼管, (標稱150mm, 厚5.0mm), 樓板套管裝設	個		1510542F3#
	管及管件, 配管用碳鋼鋼管, 鍍鋅鋼管, (標稱200mm, 厚5.8mm), 樓板套管裝設	個		1510542H3#
	管及管件, 配管用碳鋼鋼管, 鍍鋅鋼管, (標稱250mm, 厚6.6mm), 樓板套管裝設	個		1510542K3#
	管及管件, 配管用碳鋼鋼管, 鍍鋅鋼管, (標稱300mm, 厚6.9mm), 樓板套管裝設	個		1510542L3#
	管及管件, 配管用碳鋼鋼管, 鍍鋅鋼管, (標稱350mm, 厚7.9mm), 樓板套管裝設	個		1510542M3#

2. 選取設定好的 Excel 檔，會自動讀取模型中的元件，與 Excel 資料進行比對。

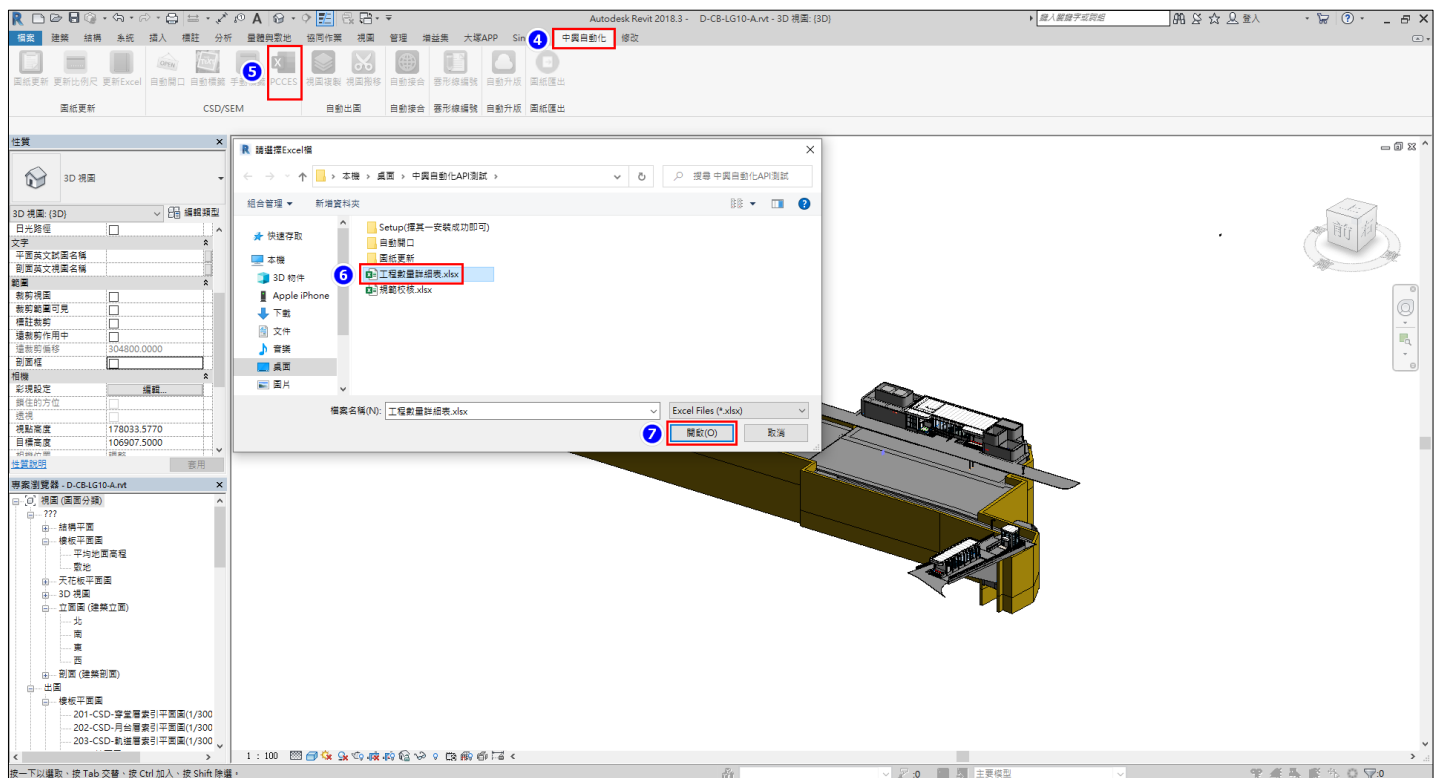

3. 自動生成數量計算表，於對照的 Excel 資料夾中。

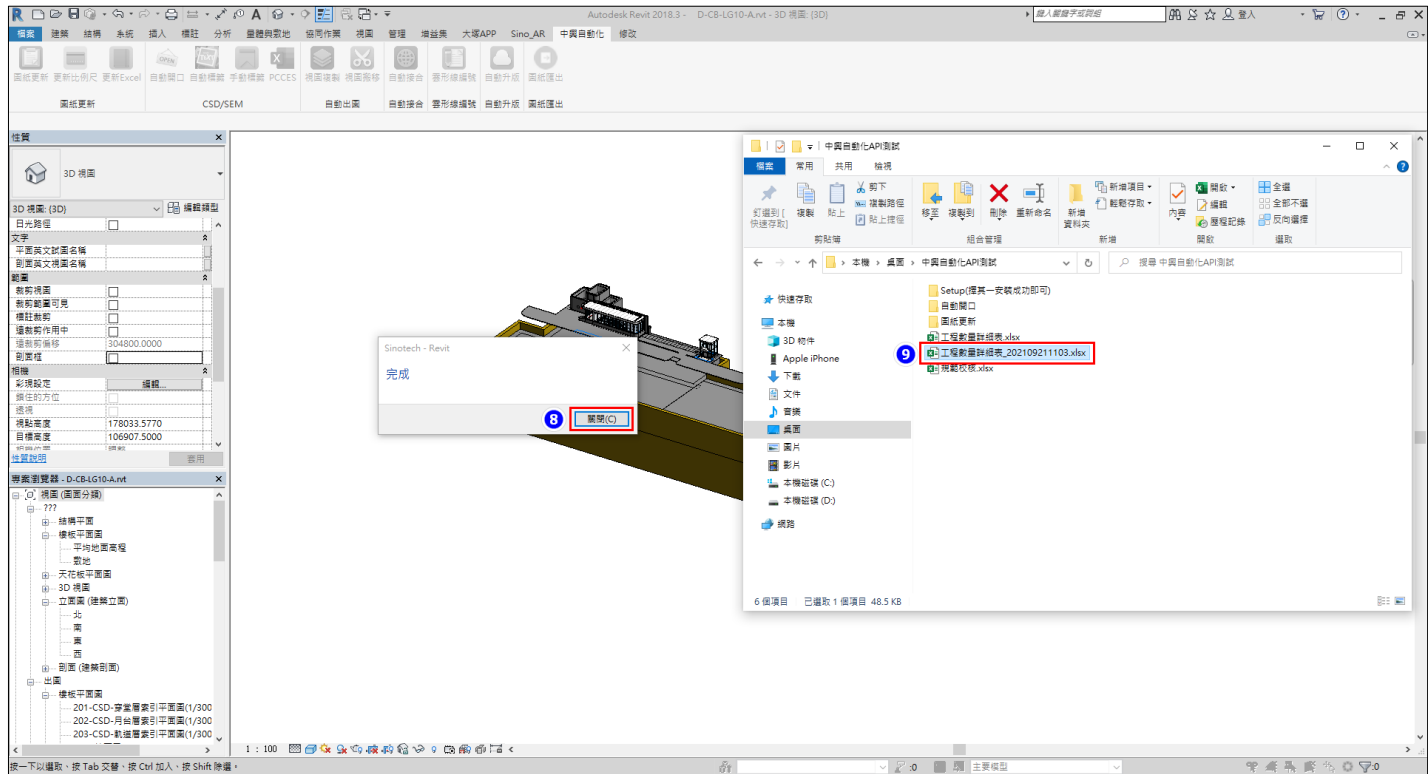

4. 於「工程數量計算表」、「工程數量詳細表」中，將模型中的元件資料填入完成。

[illegible]